

BY

VISHNU S

INTERIOR DESIGN

PORTO
FOLIO





VISHNU S

ABOUT ME

Enthusiastic and qualified Interior Designer seeking job opportunities. Skilled in meeting client expectations and delivering innovative designs. Eager to contribute to company success through creative challenges



8668171839



vishnus1602@gmail.com



2, Bharathiyan street,
Modakkurichi, Erode - 638104.

EDUCATION

Bachelor of Philosophy - 2020-2023
University of Madras

Diploma in Interior Design - 2023-2024.
Bangalore School of Design & technology.

CERTIFICATION

Interior Design (Short Course)
XFord Home Study centre - 2023-2024

SKILLS

Technical Skills

- Auto CAD
- Photoshop
- SketchUp
- Requirement and Gathering

Hard Skill

- CAD Designing
- SketchUp Designing
- Sketching
- Attention to Details

LANGUAGES

- English
- Tamil

PROJECTS



1. KITCHEN

Presented a Project on "Kitchen Detaling" in 12x7 Square ft in Kitchen Detailing with AutoCAD and SketchUp.


2.BEDROOM & TOILET

Presented a Project on “Bedroom & Toilet” in 15x14 square ft in bedroom & toilet detailing with AutoCAD & SketchUp.


3.CAFE

Presented a Project on “” in 40x30 square ft Landscaping in Cafe with SketchUp



LAYOUT OF THE HOUSE

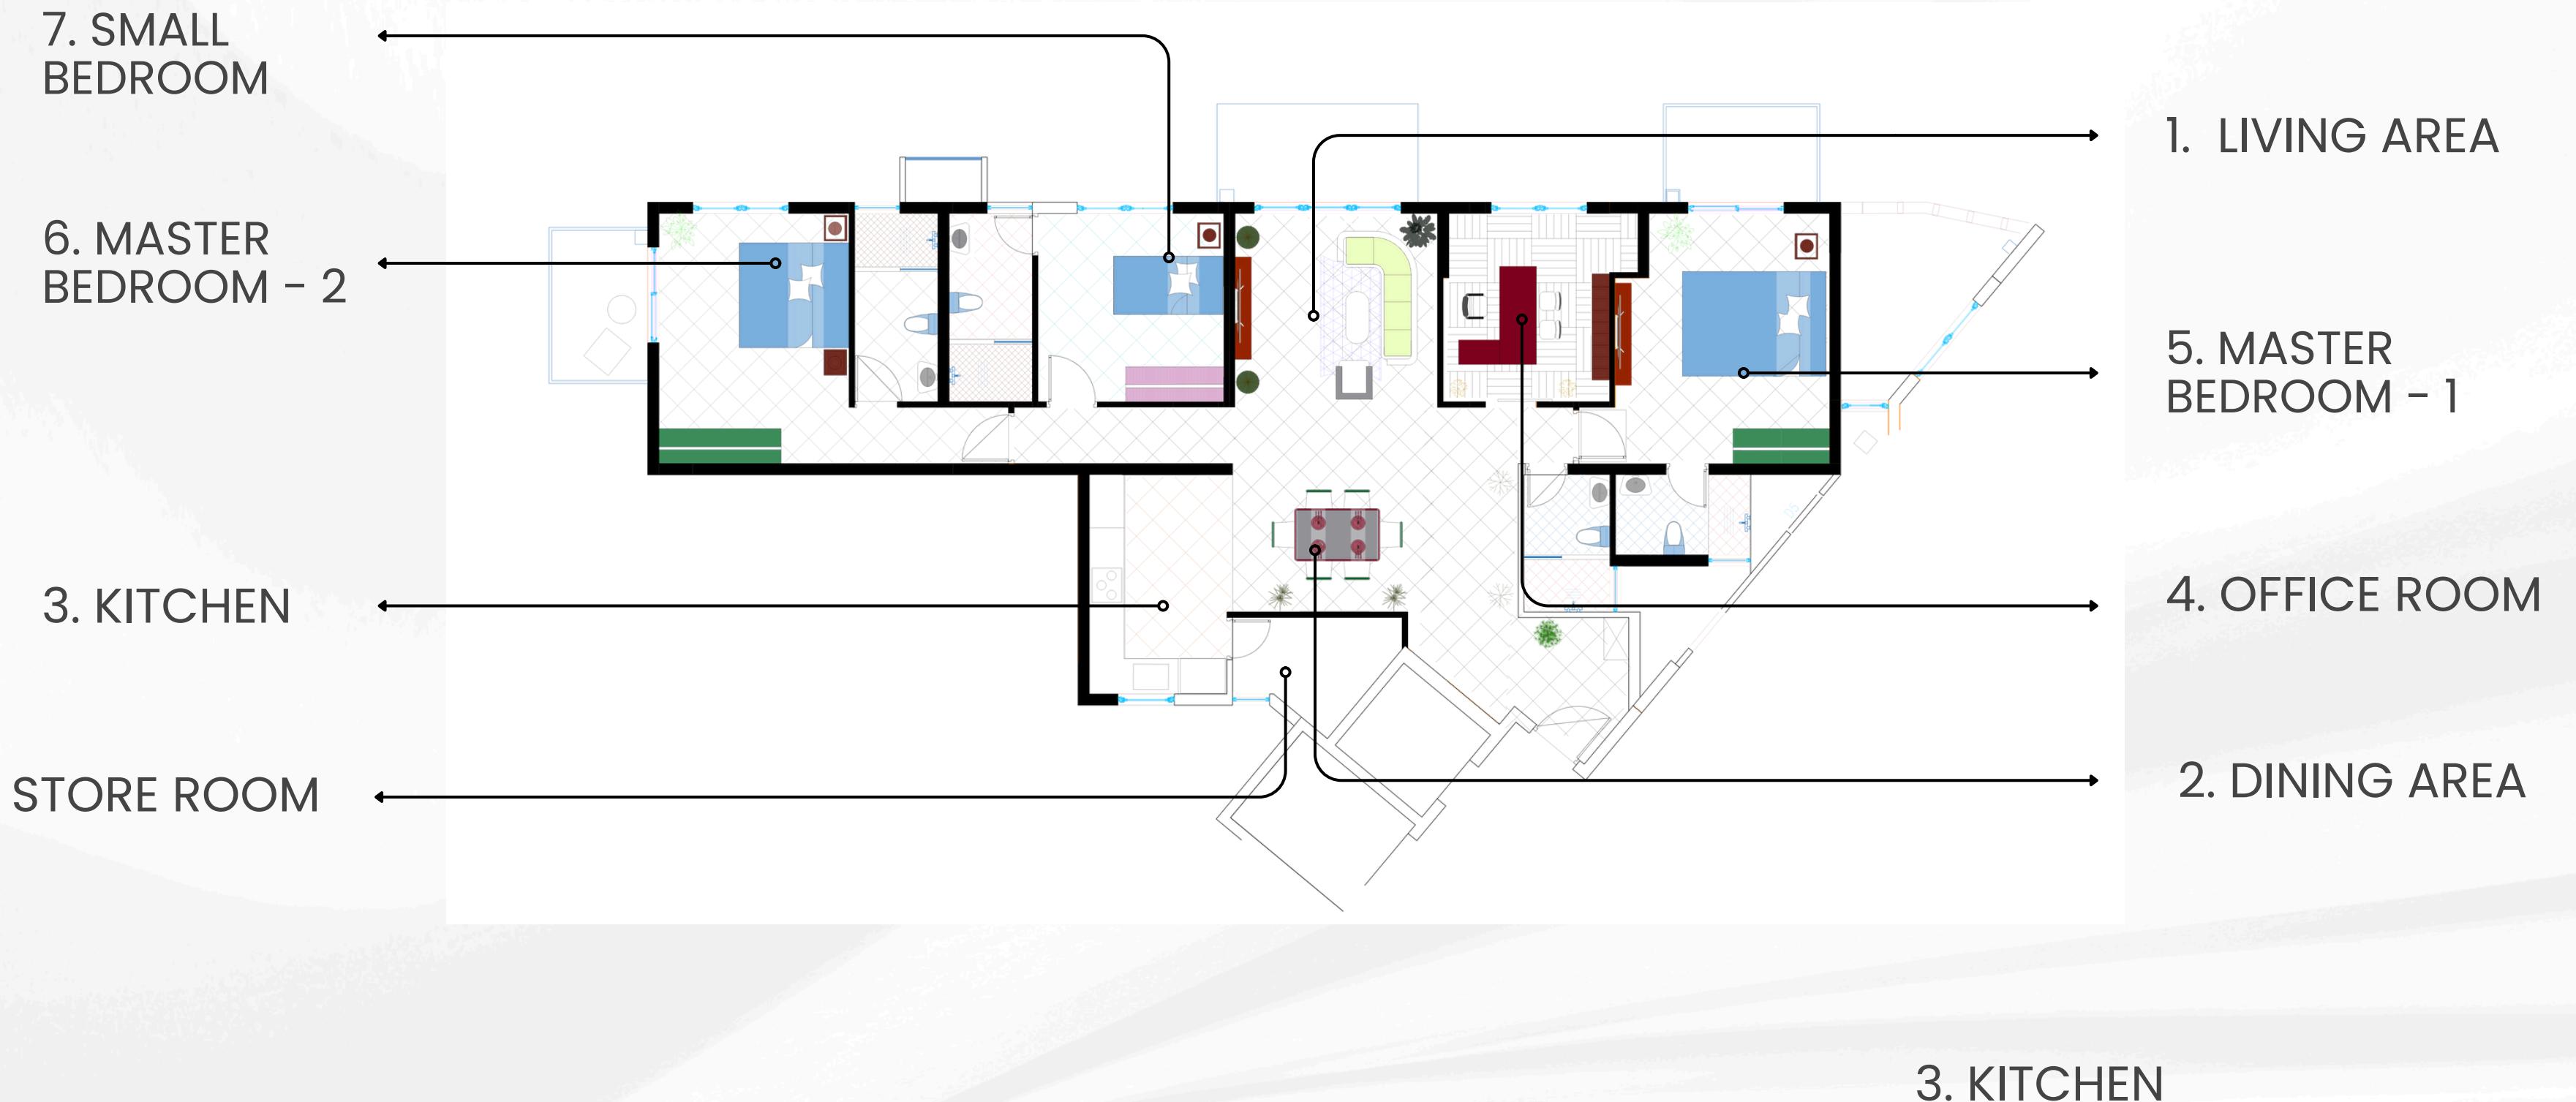

KITCHEN

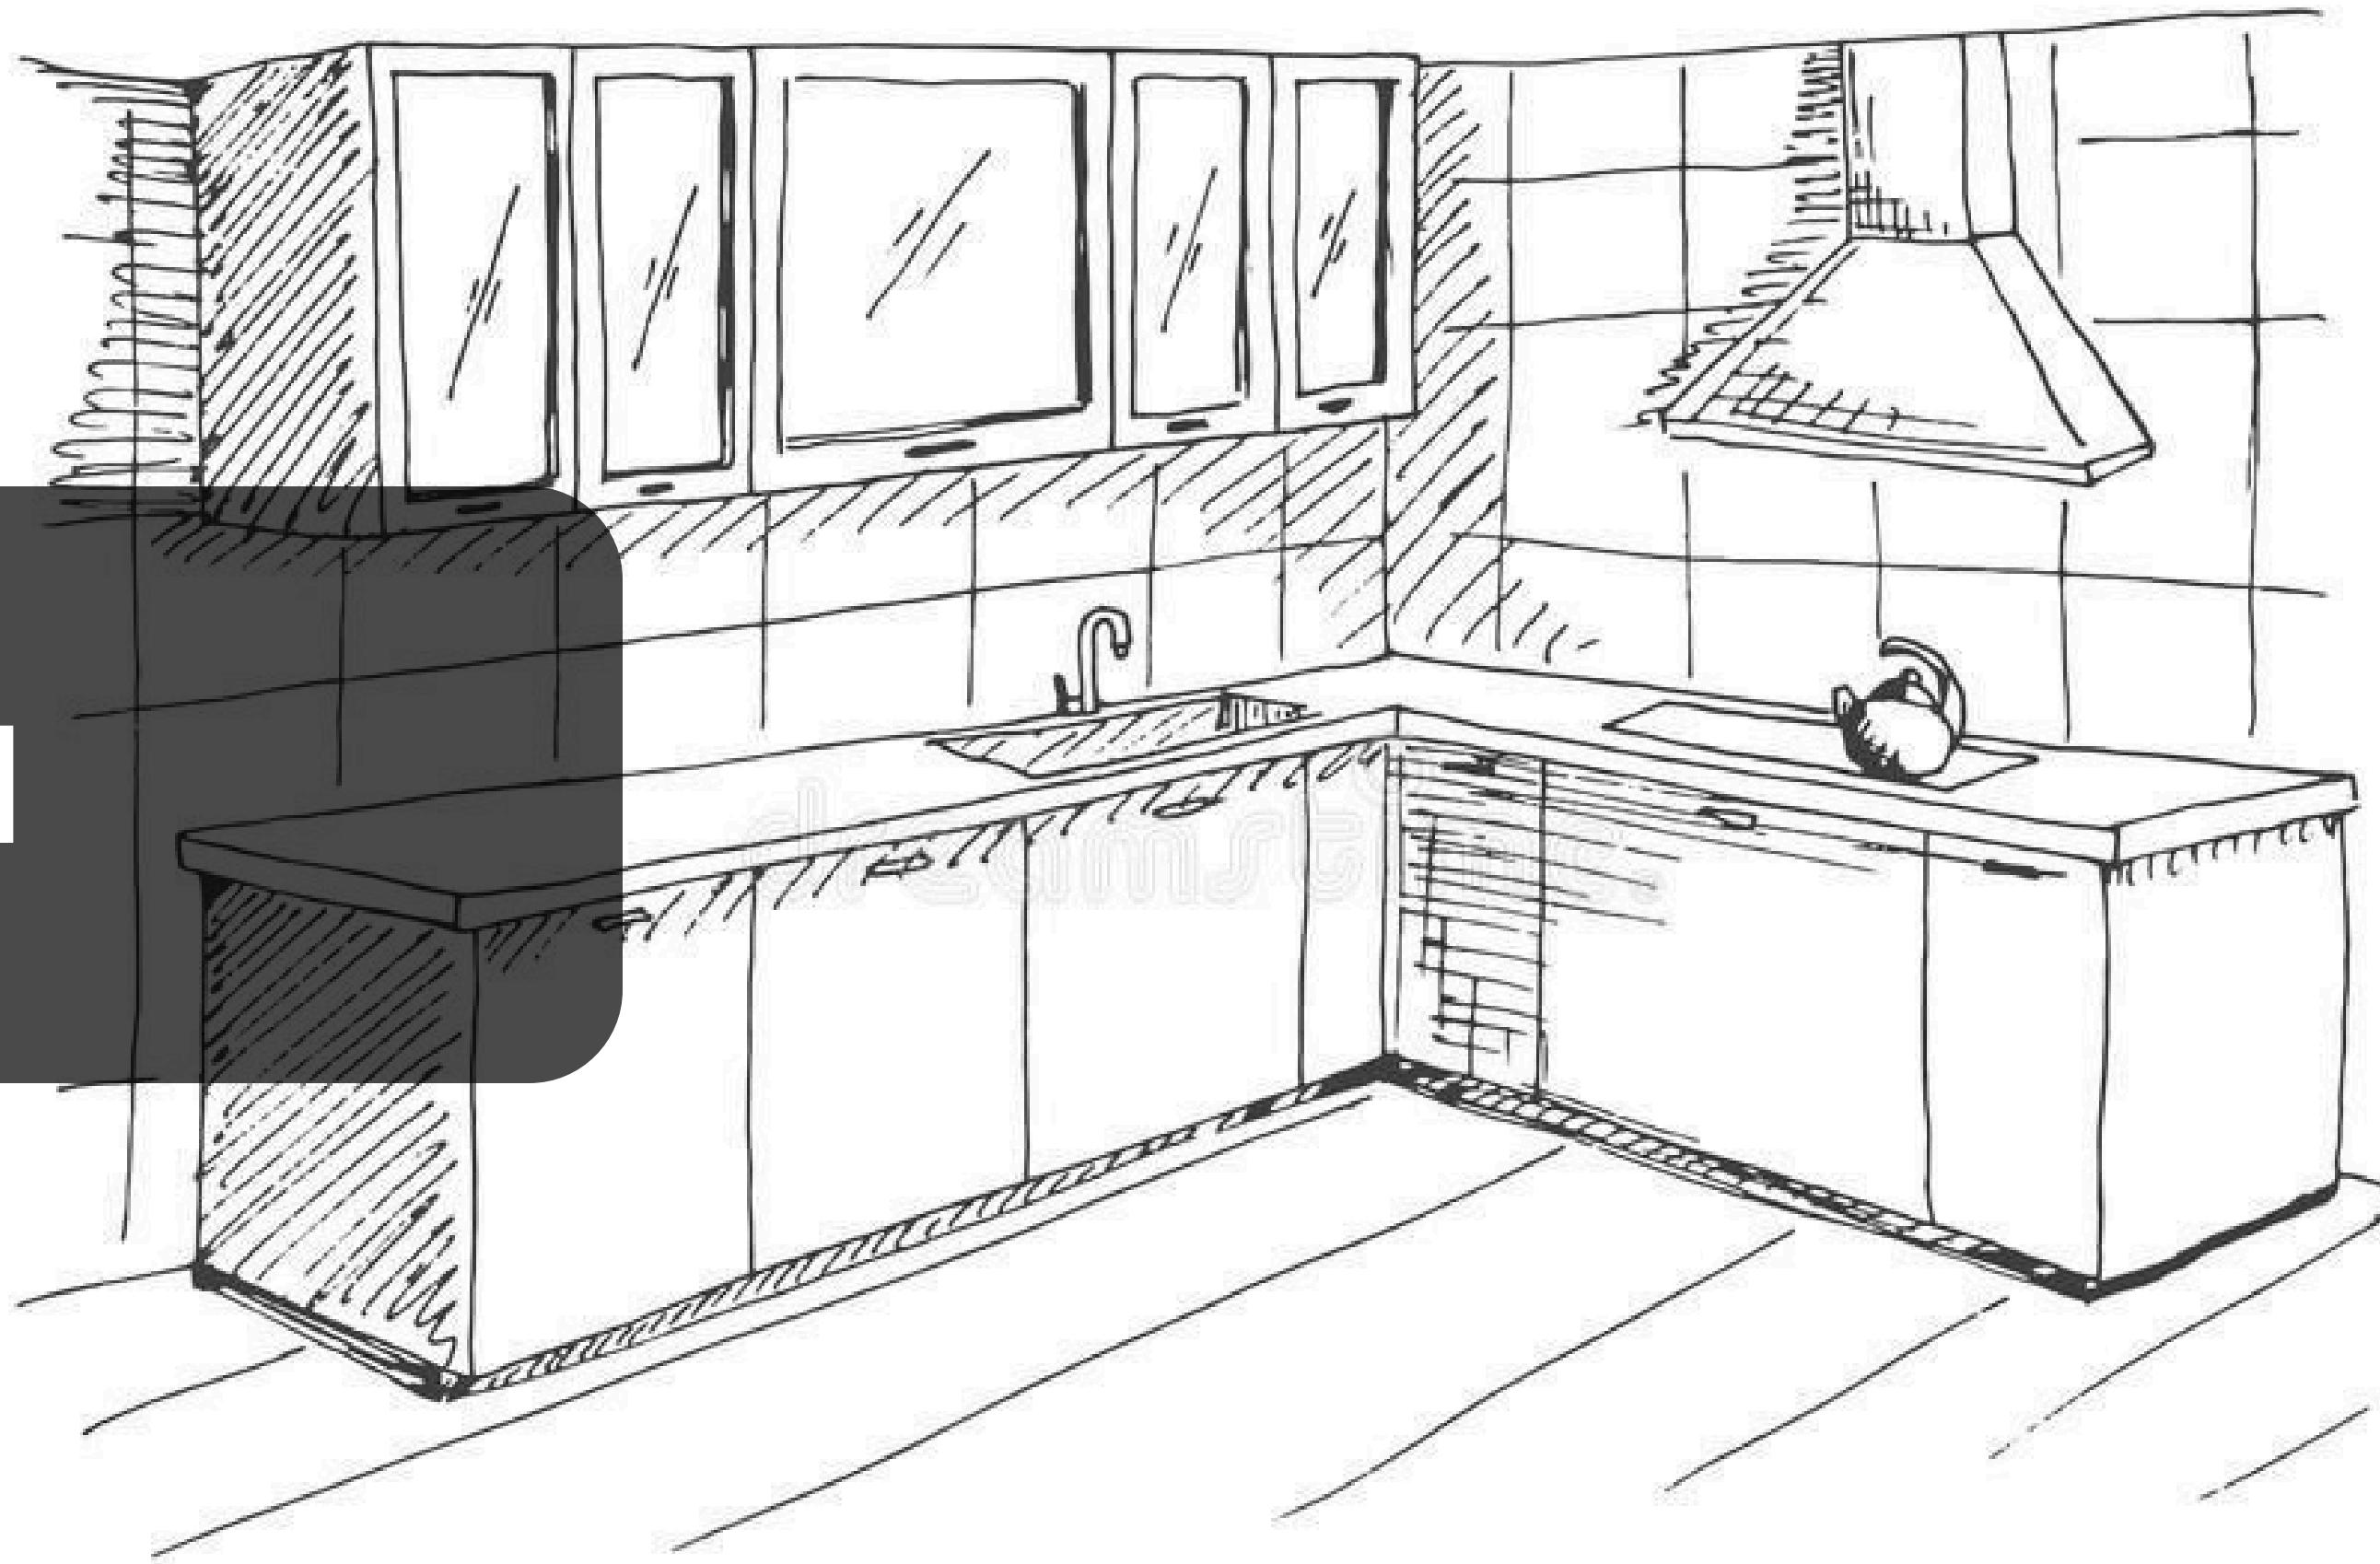


KITCHEN RENDERED IMAGE

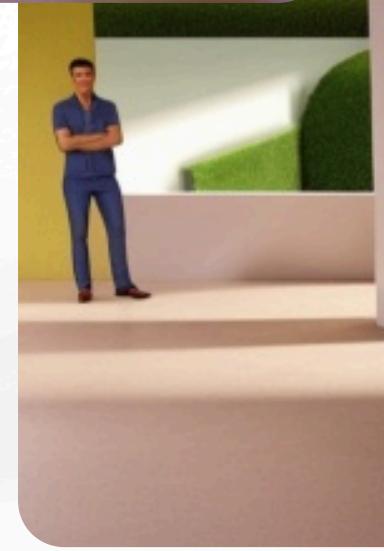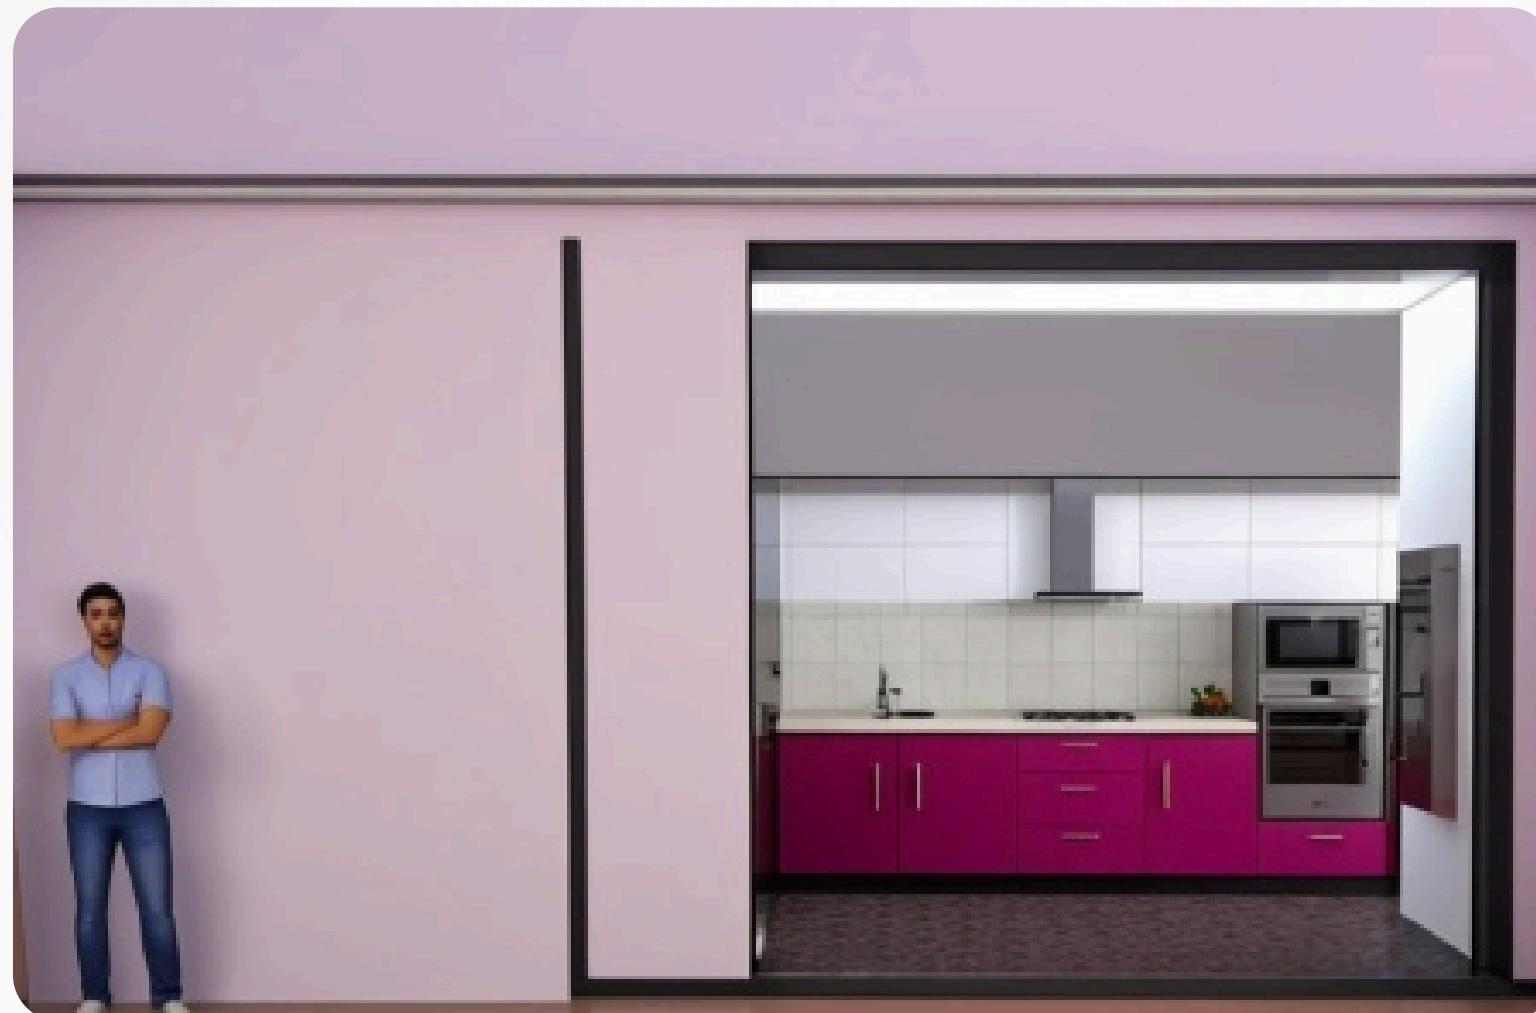


FRONT VIEW


MEASUREMENTS

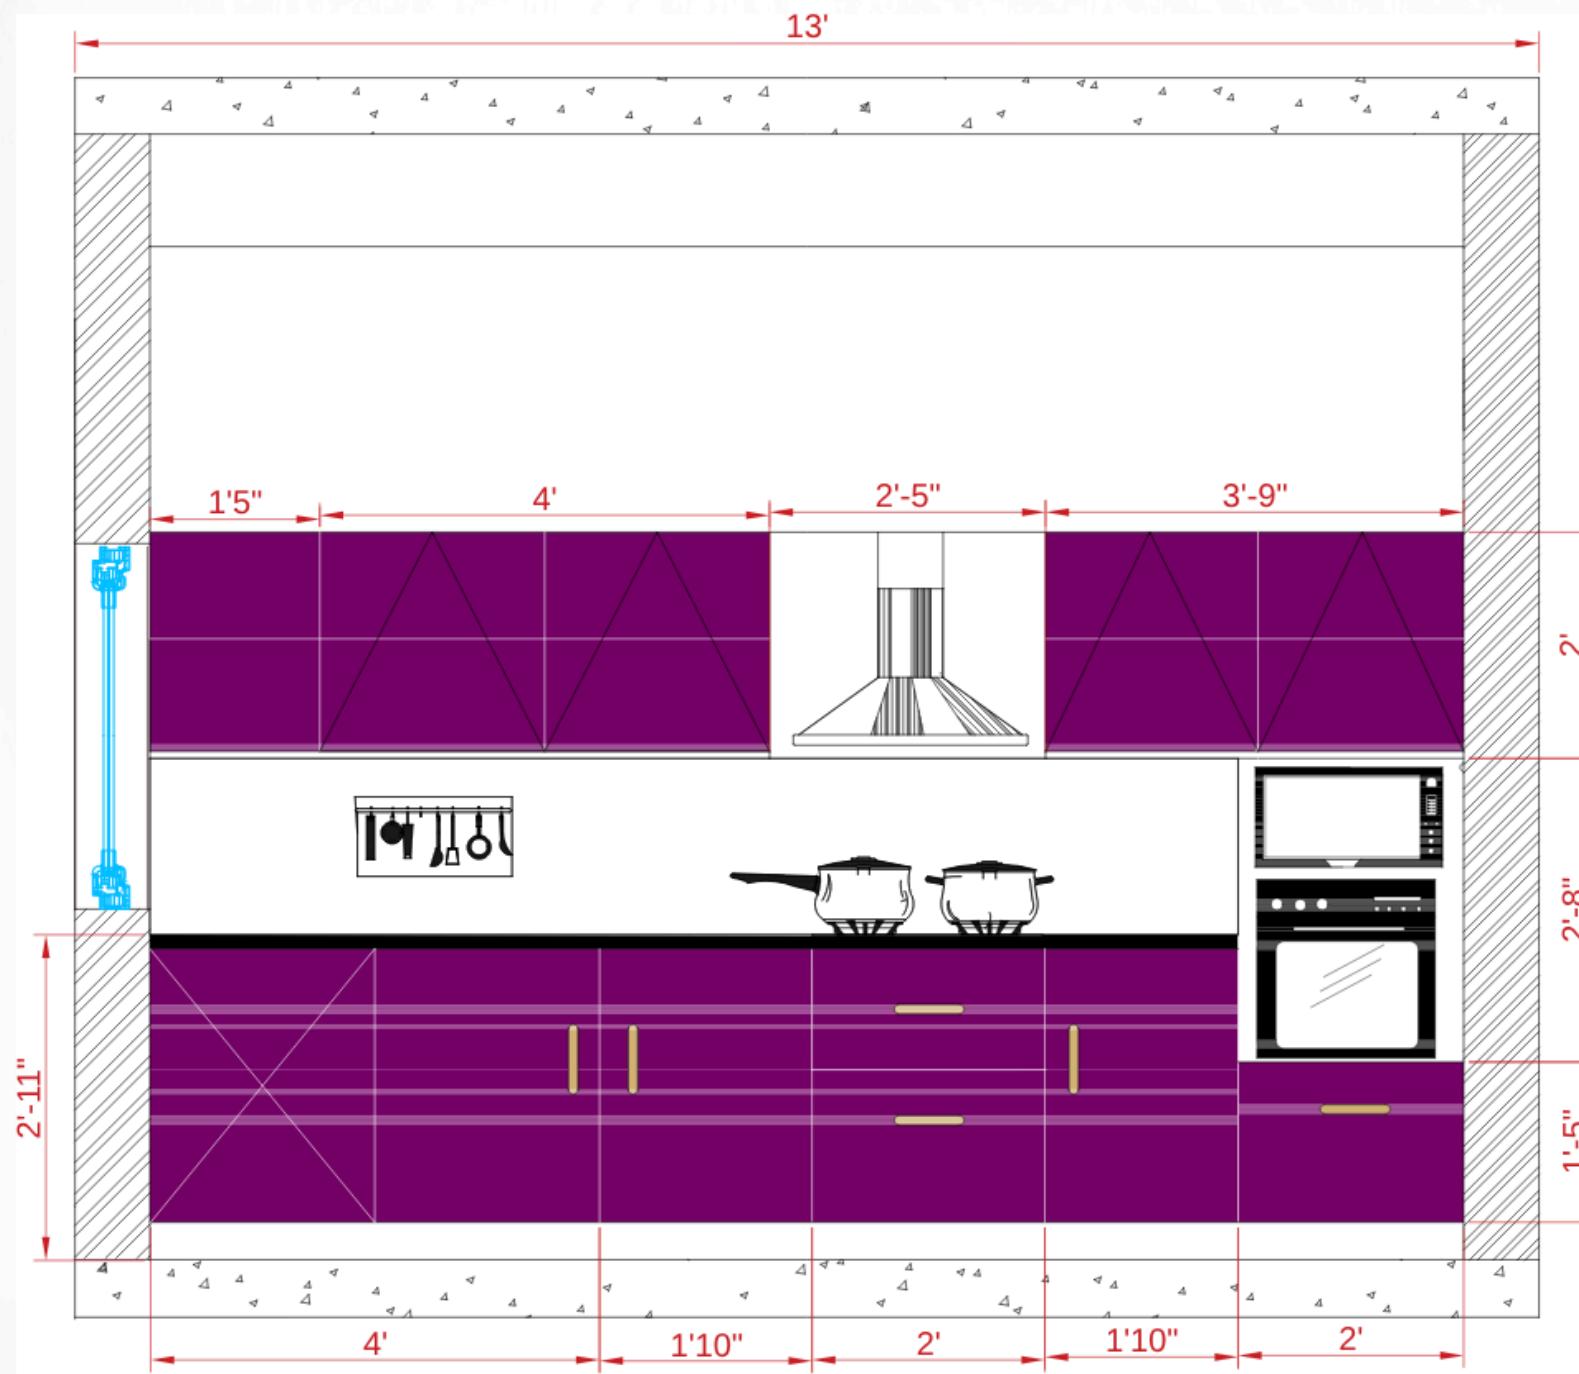

KITCHEN TOP

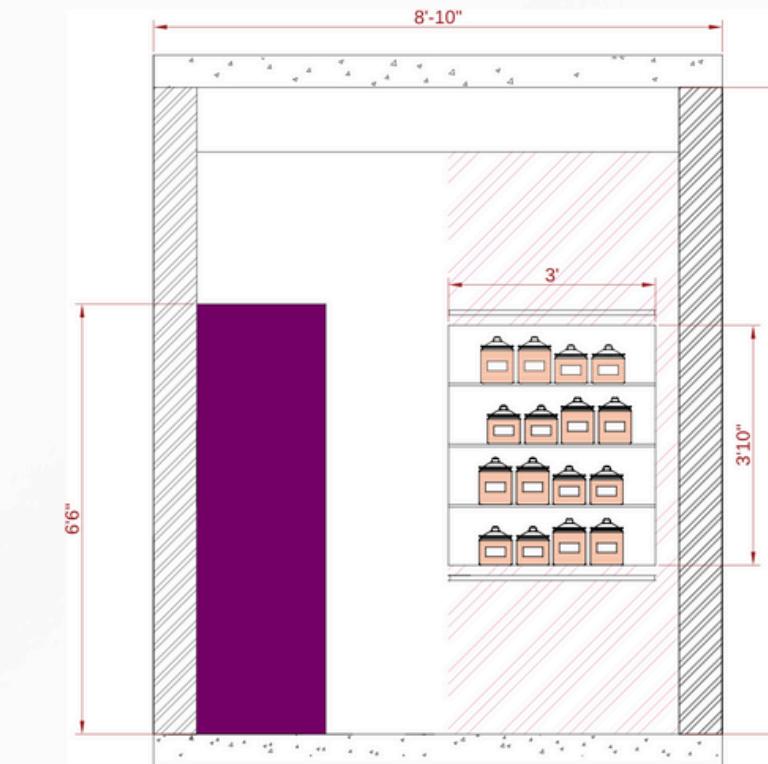


SHELF

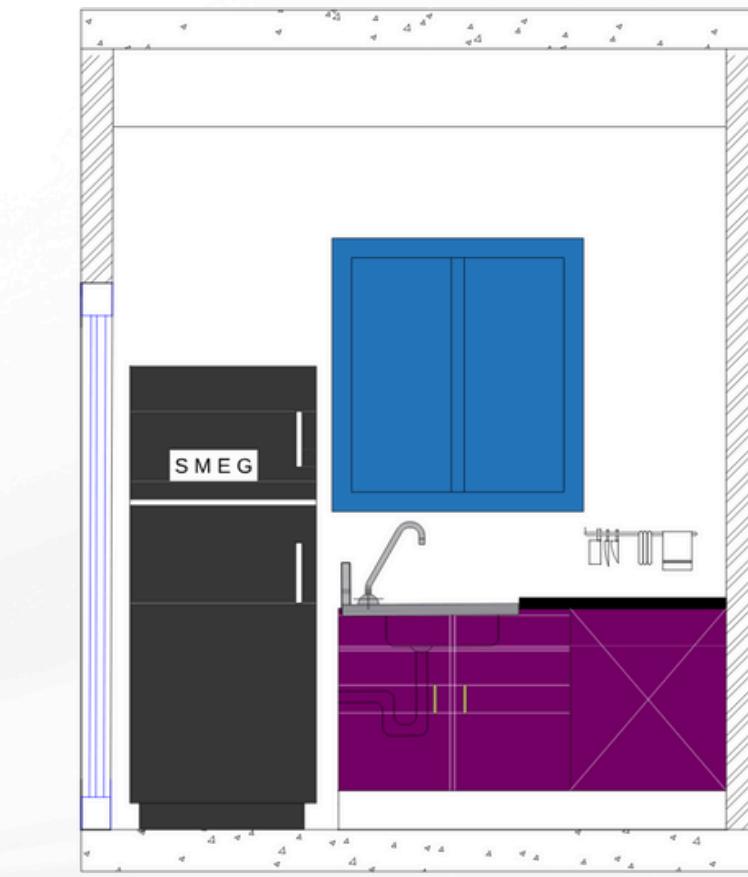

BED ROOM & BATHROOM



BED ROOM LAYOUT

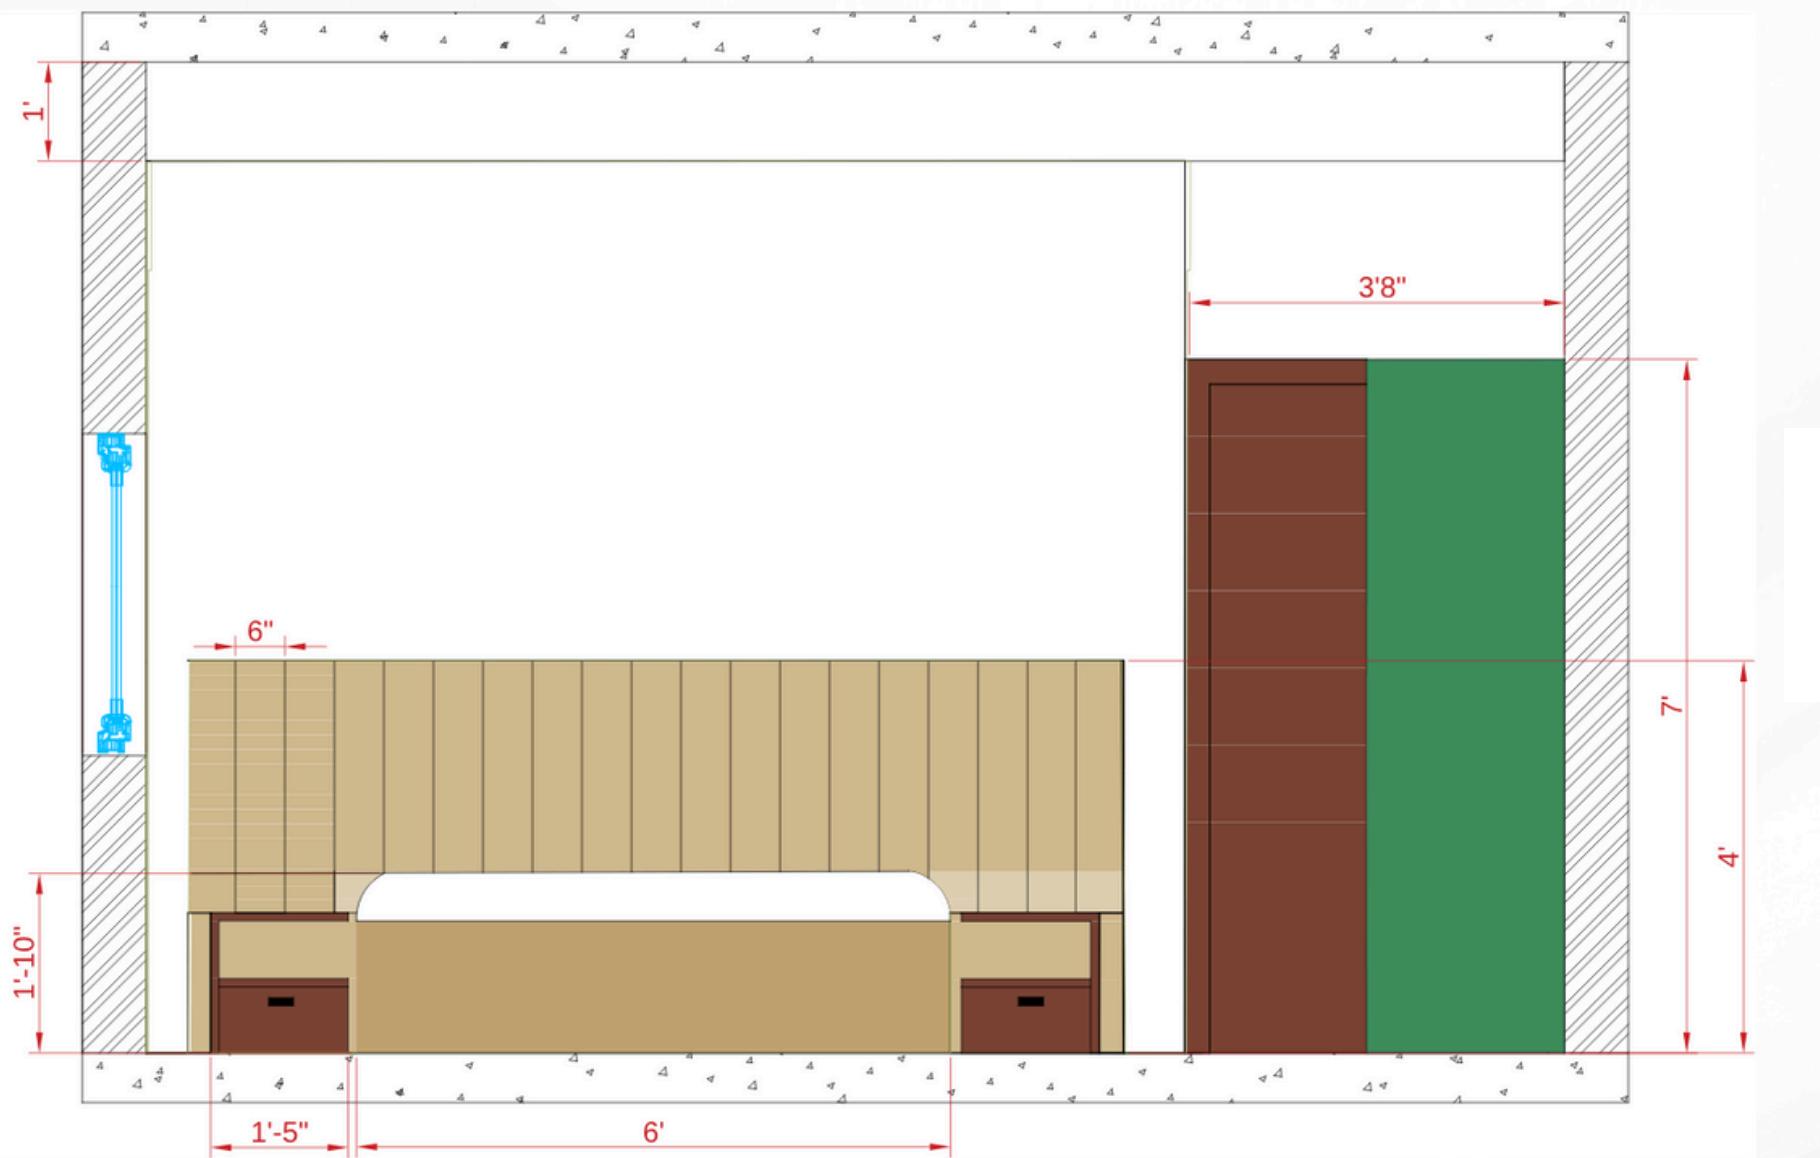

BEDROOM

Oak wood table
17x17"

MDF Fluted panel
Material: HDHMR
Thickness: 18mm






Wallpaper

Oak Wood
Thickness:
19mm
72x78"


6-inch matters

BED ROOM XRAY

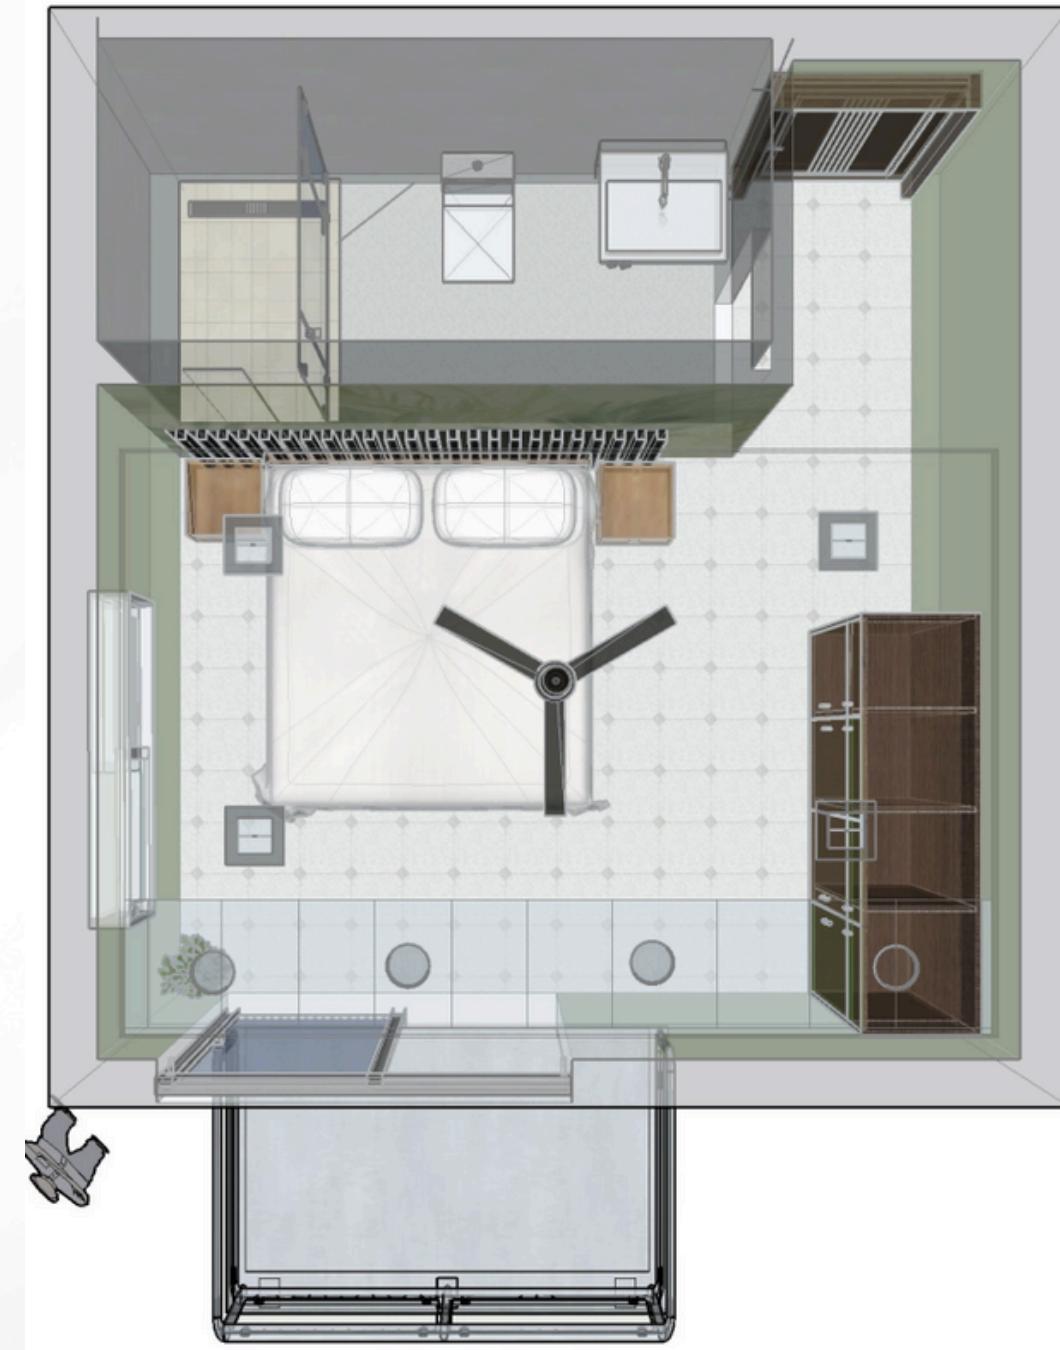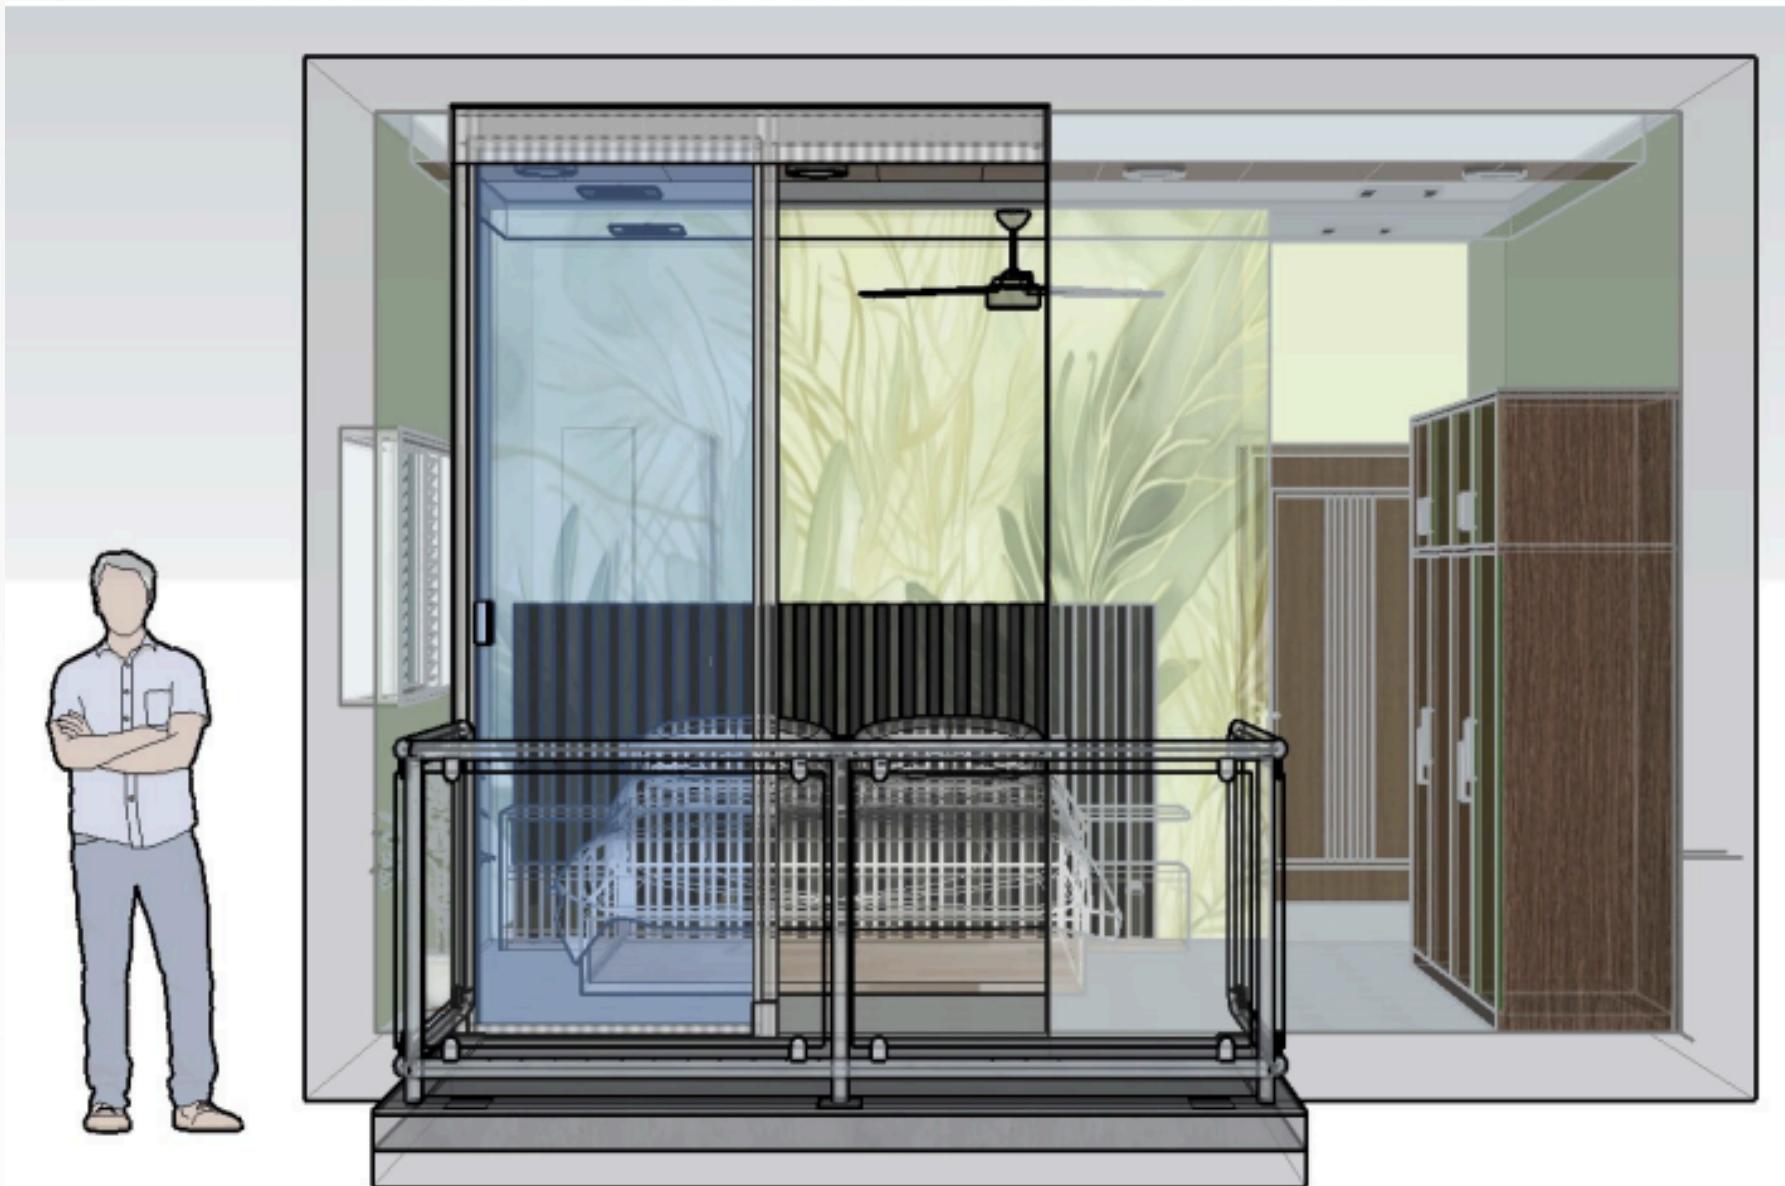


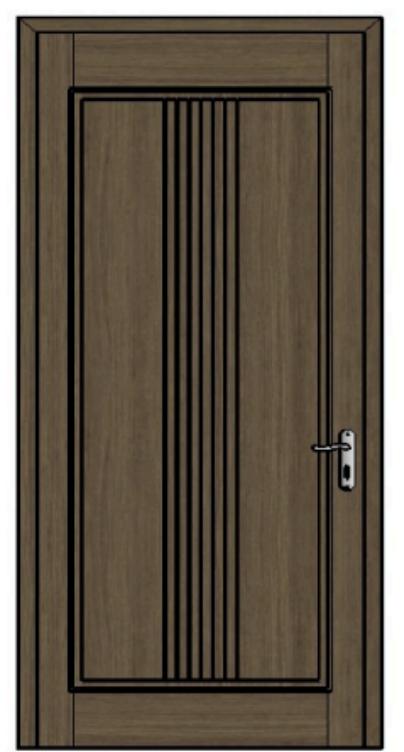



BACK VIEW

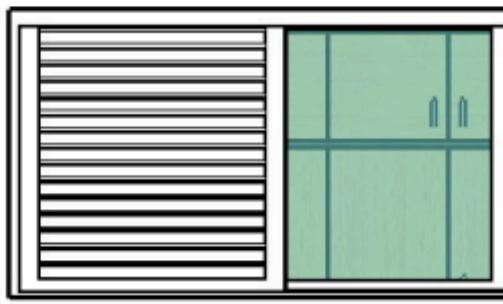

LEFT VIEW

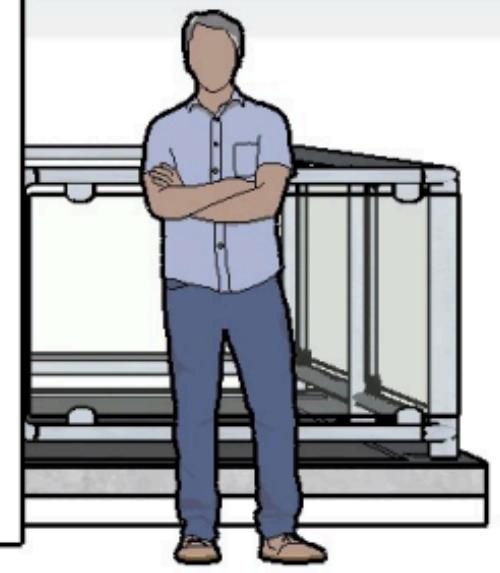


WARDROBE LAYOUT

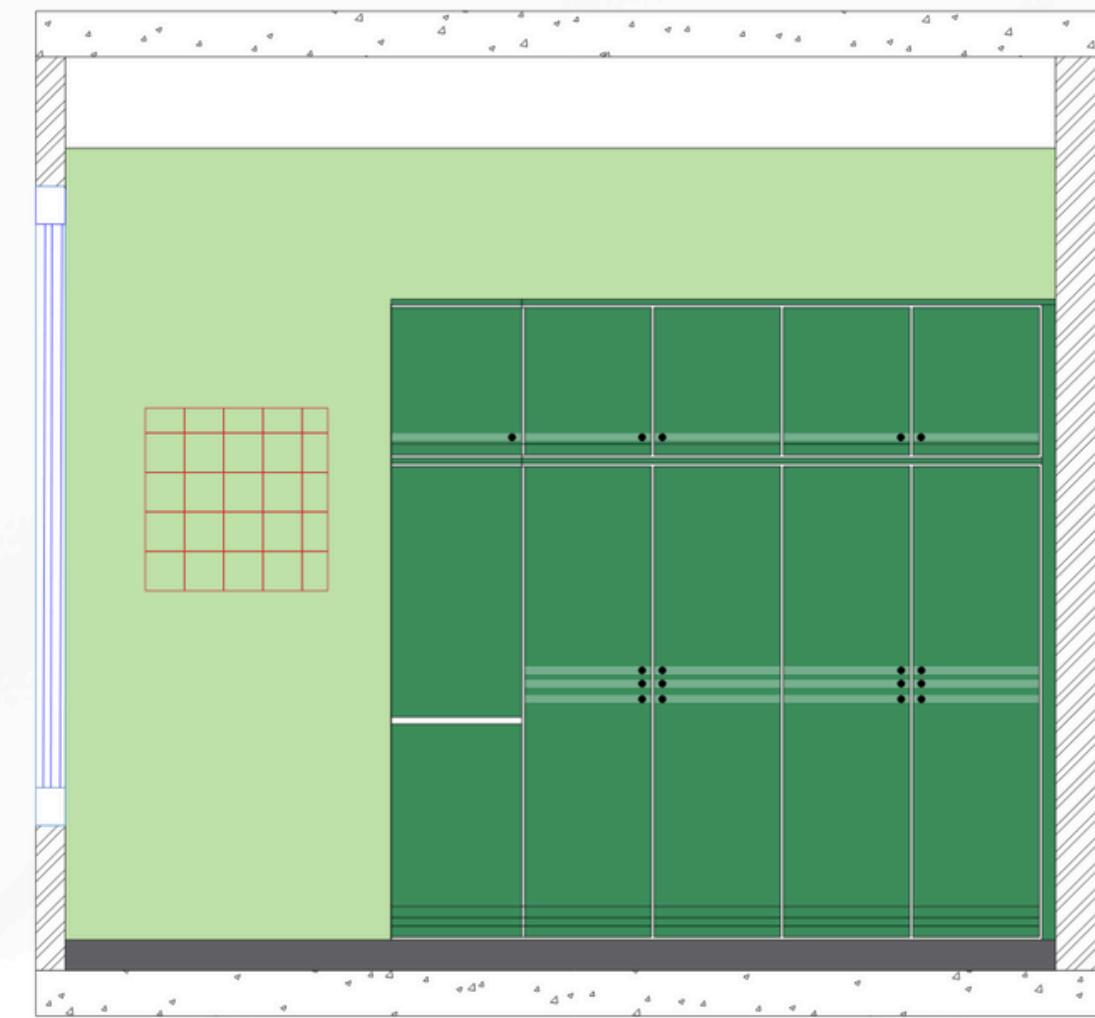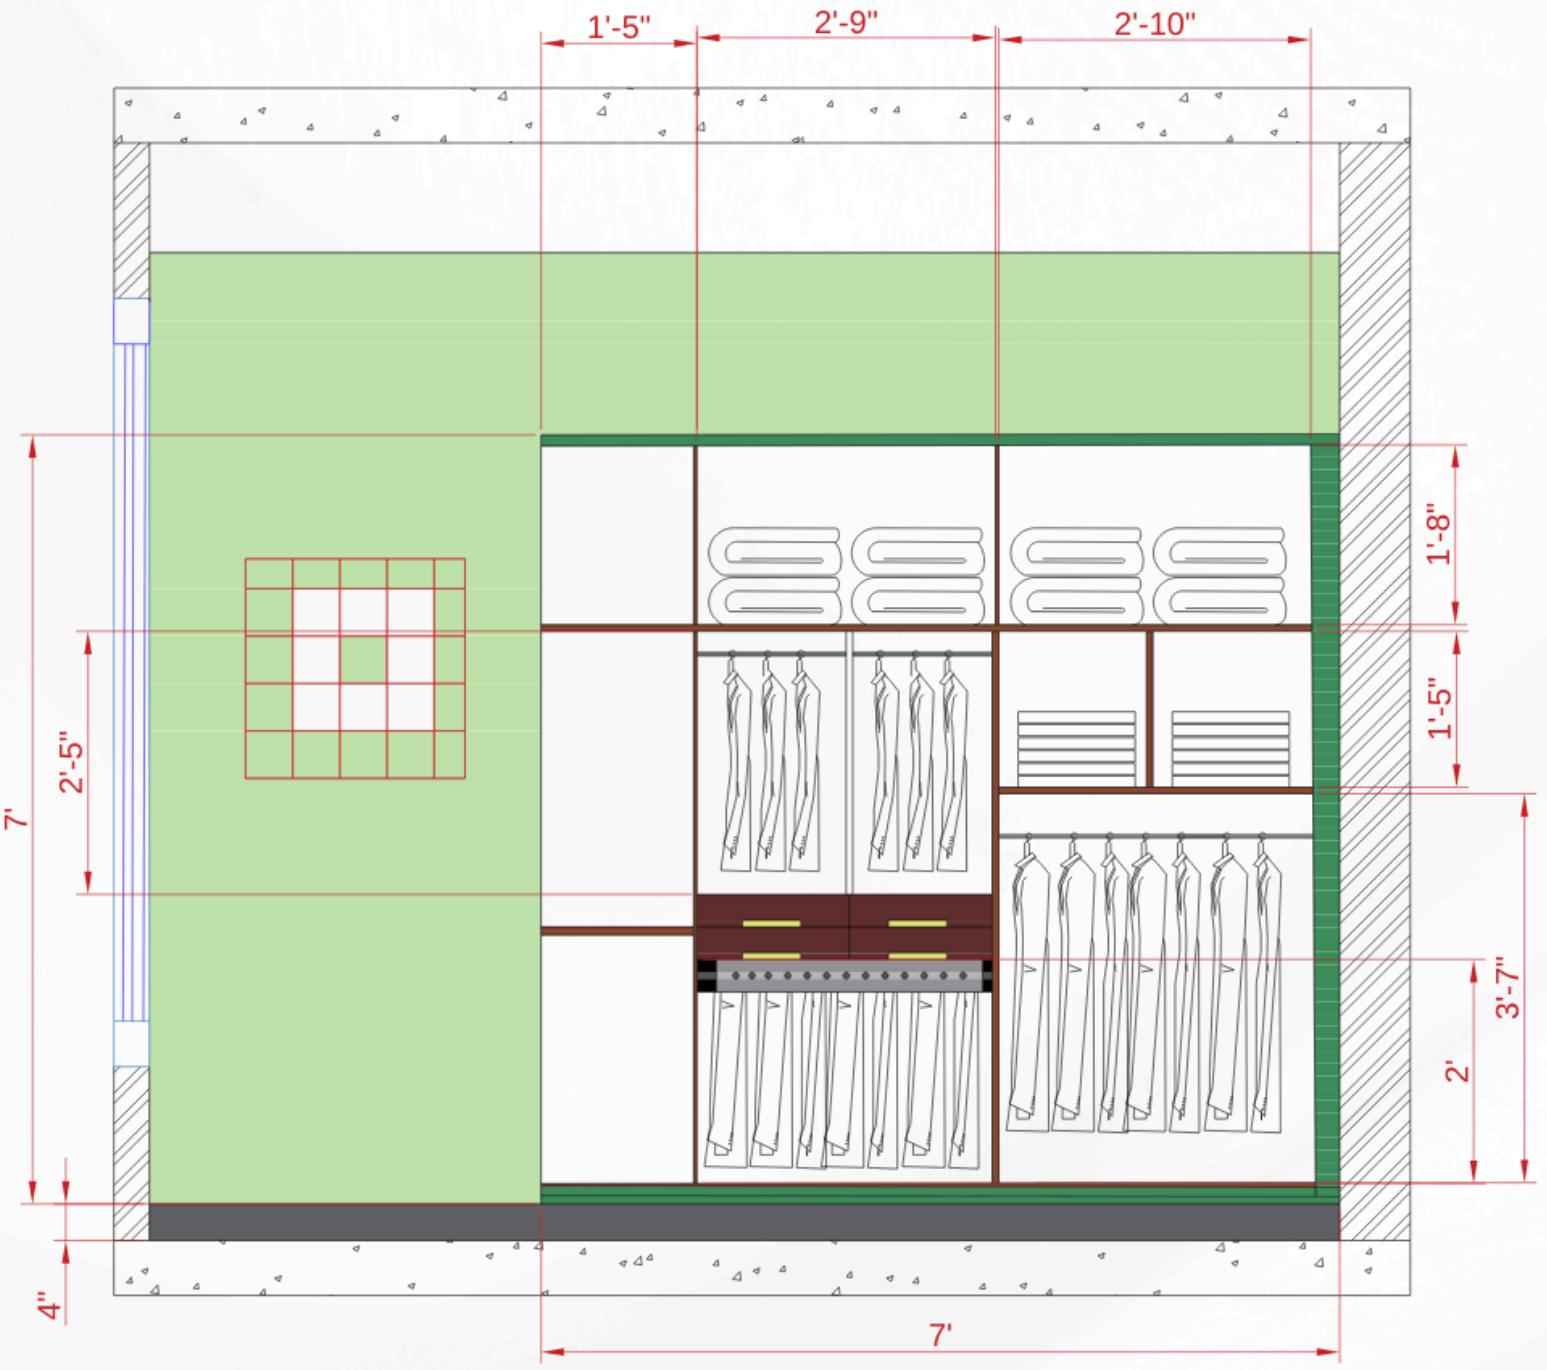



Wardrobe
7'x6'
Oak wood

Glass flute panel
Thickness: $\frac{1}{4}$ "

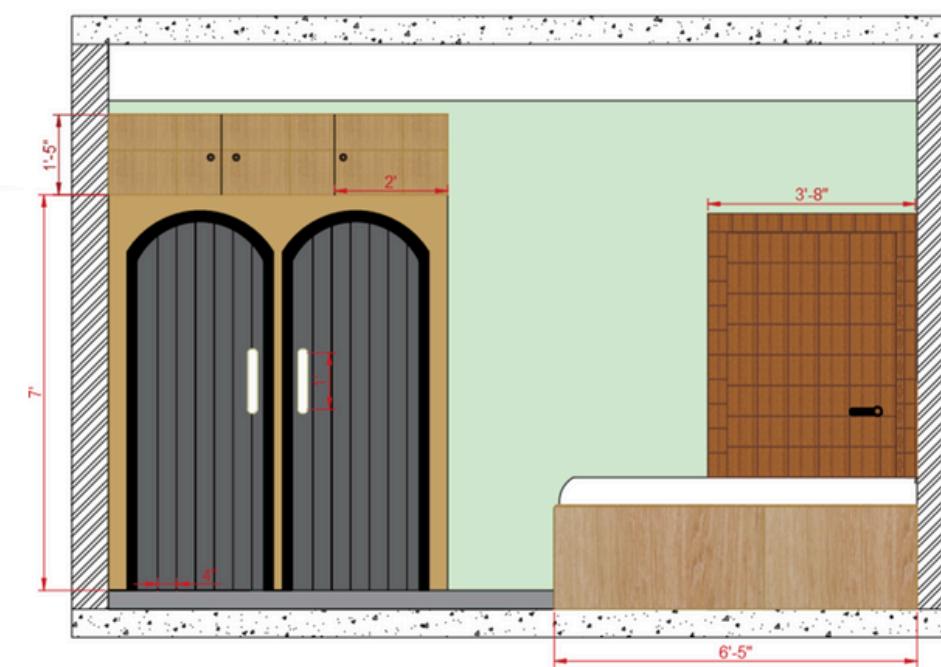


WARDROBE


BATHROOM LAYOUT

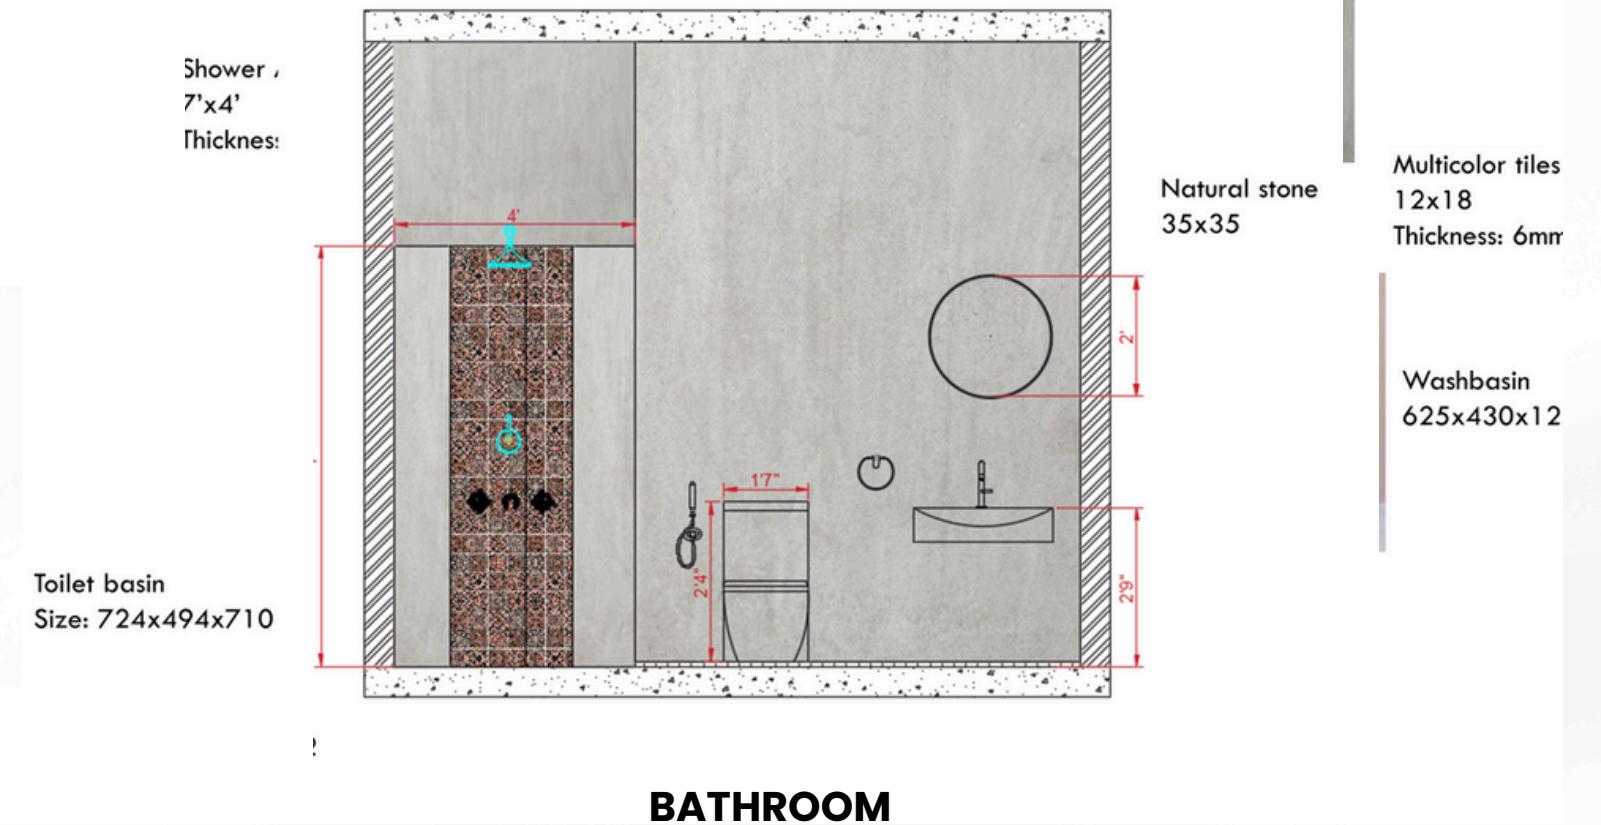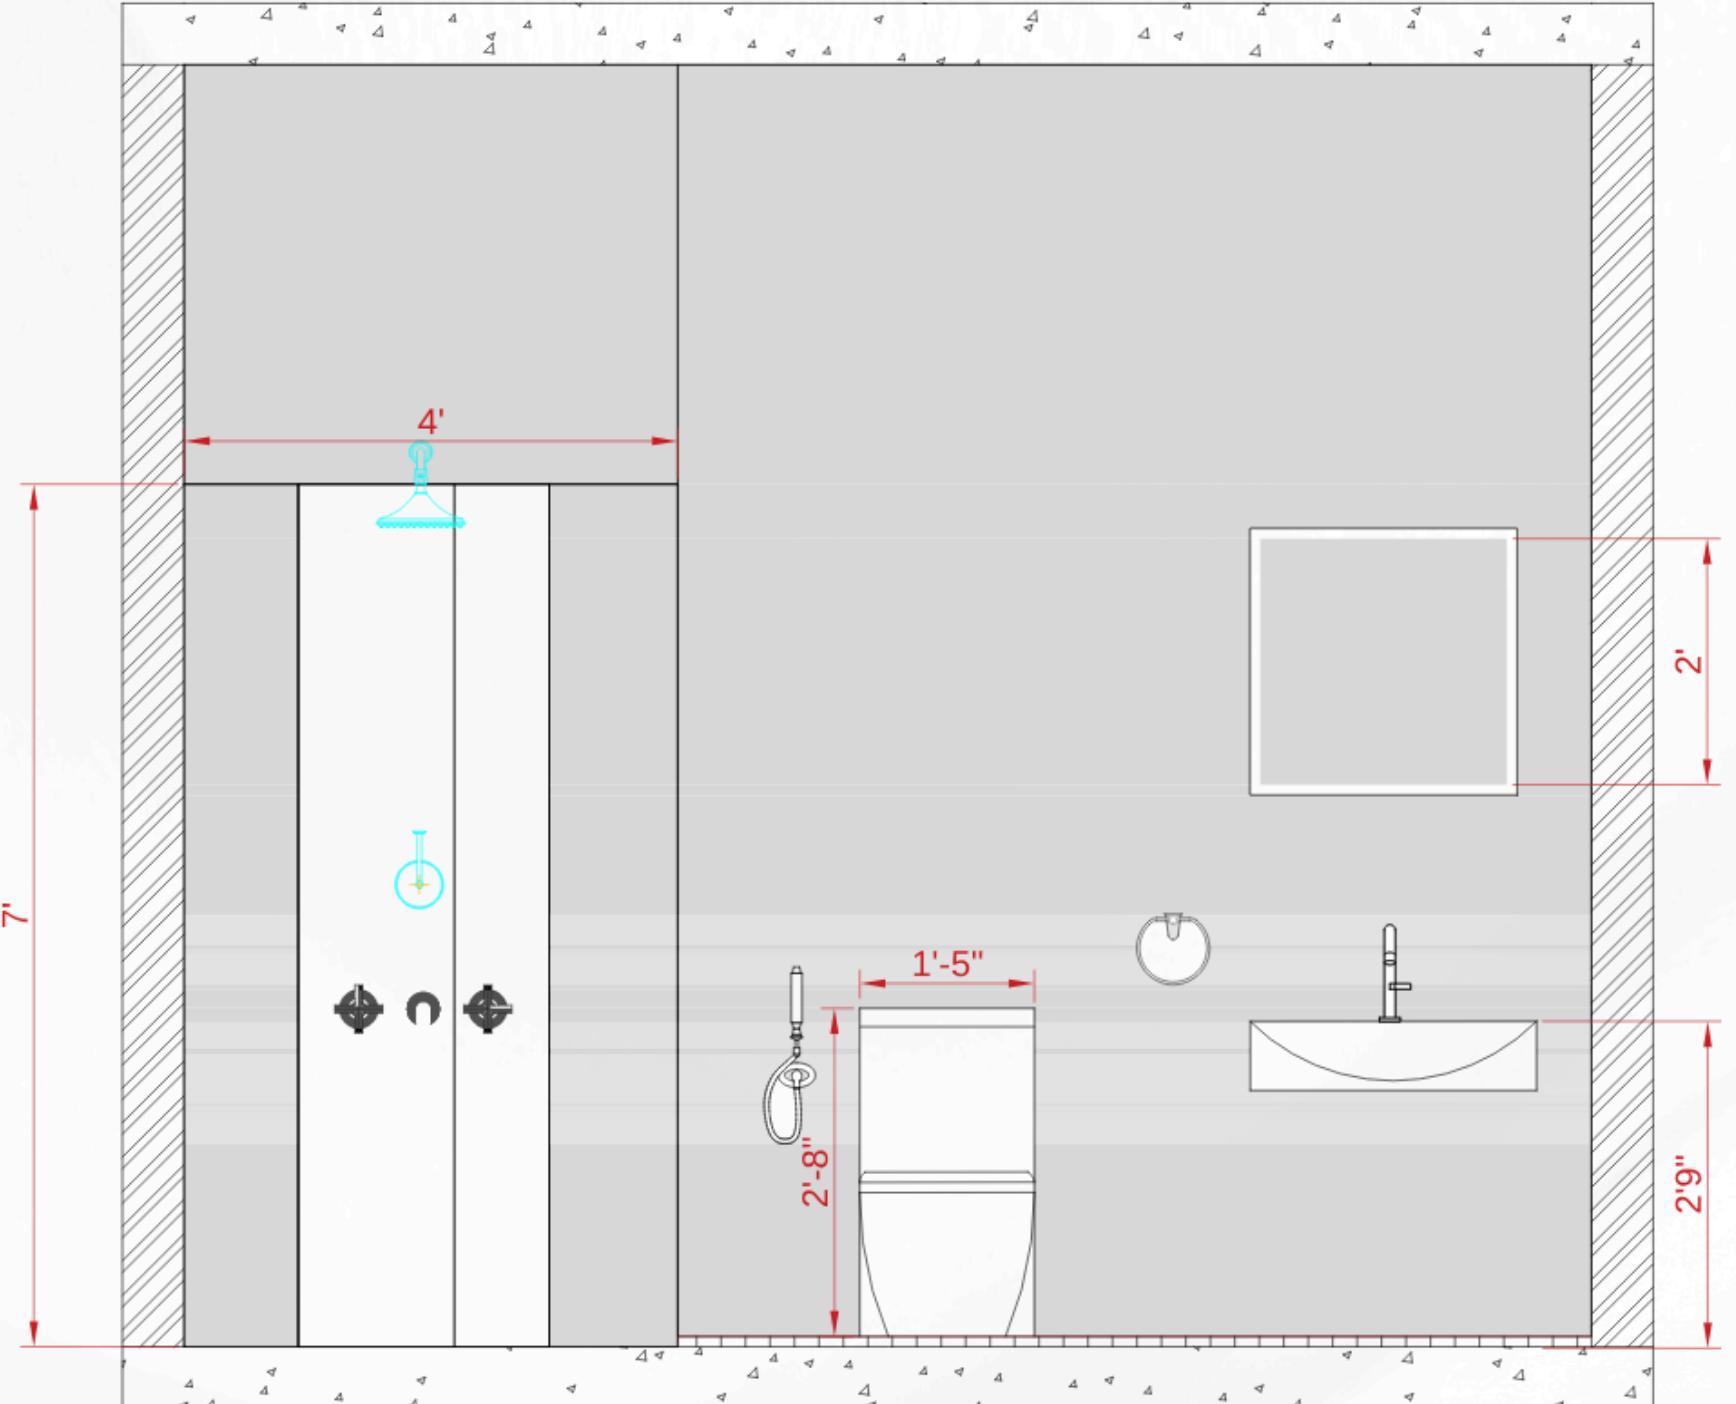


BATHROOM

FALL CEILING LAYOUT

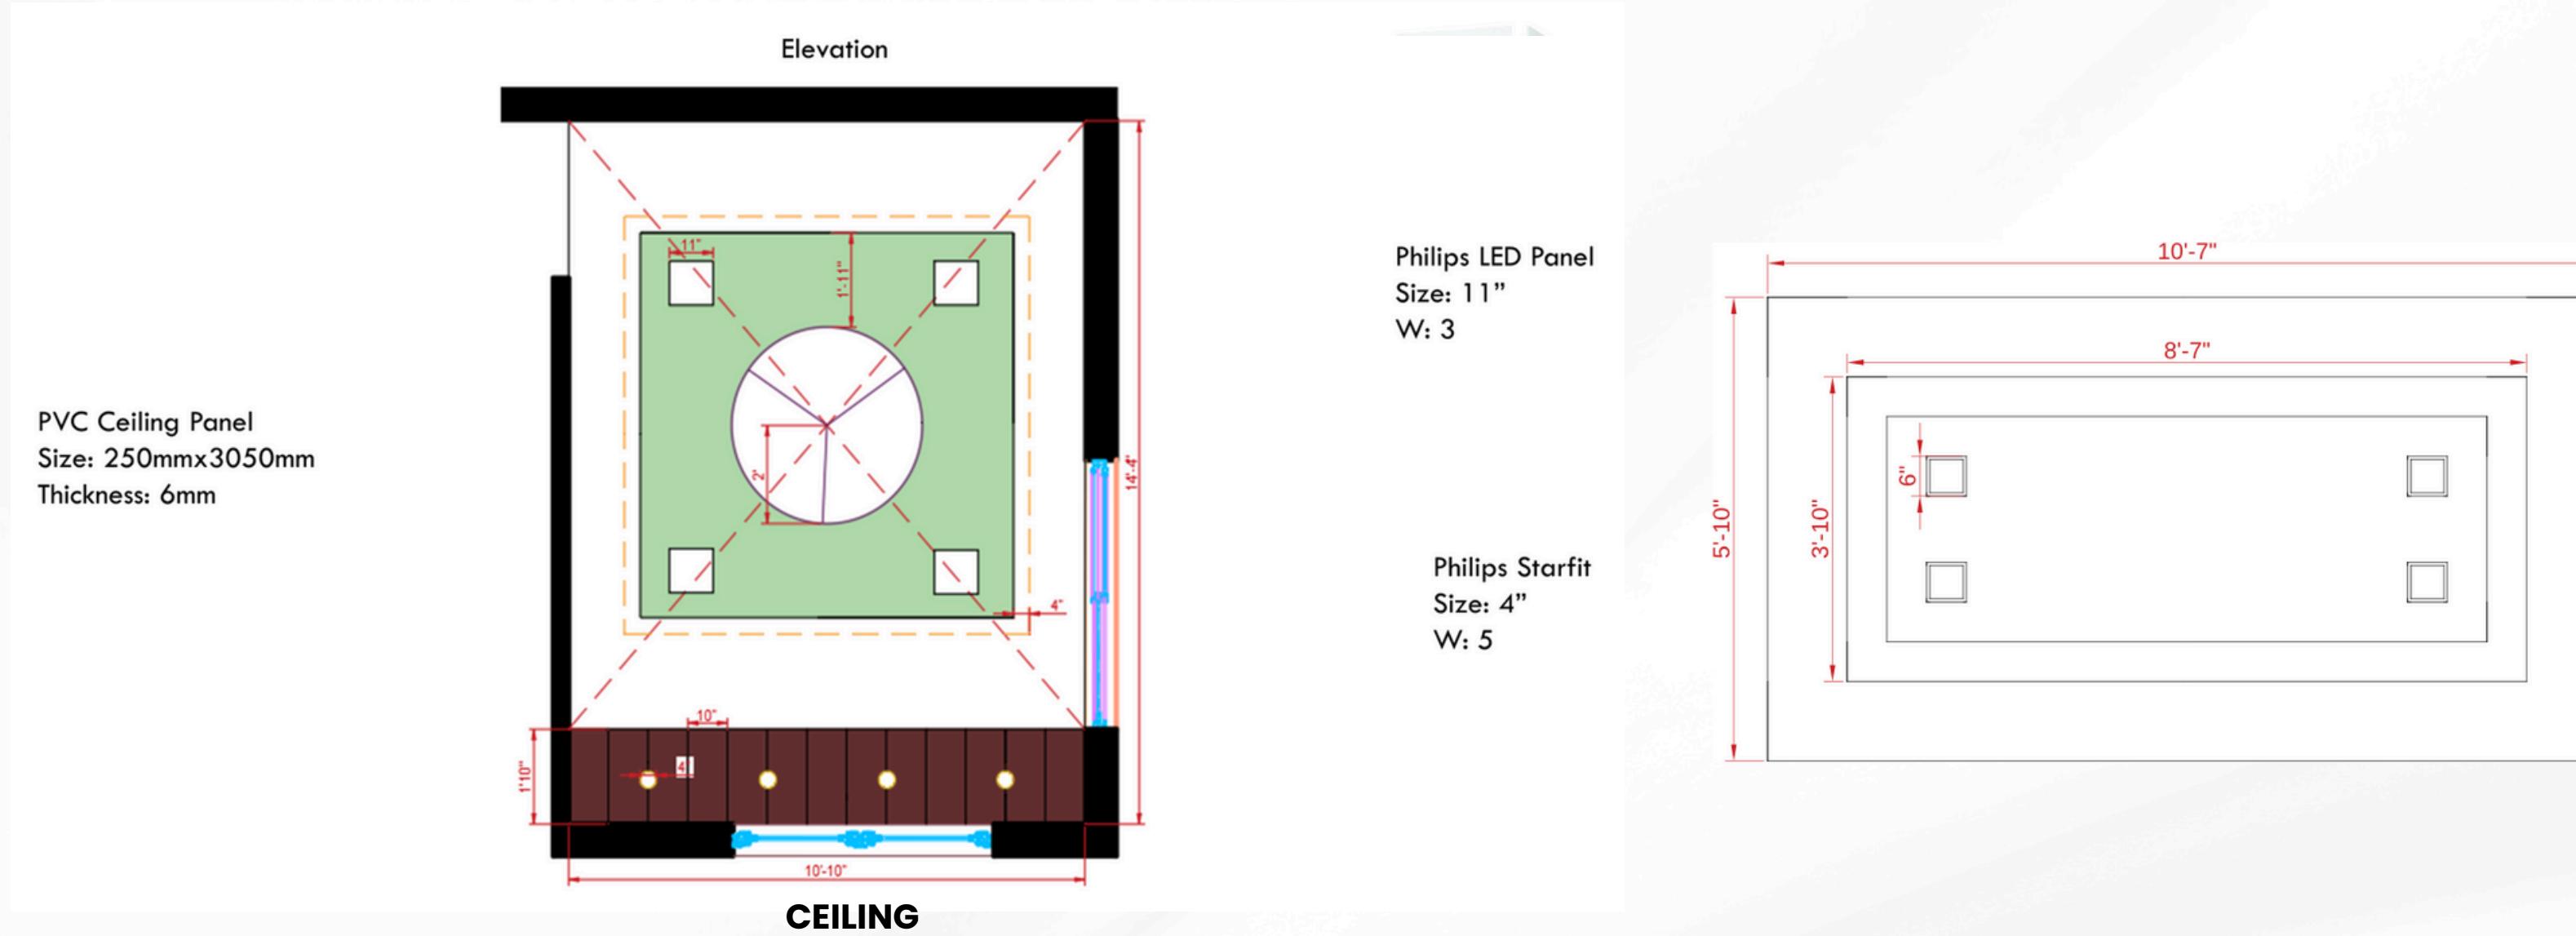

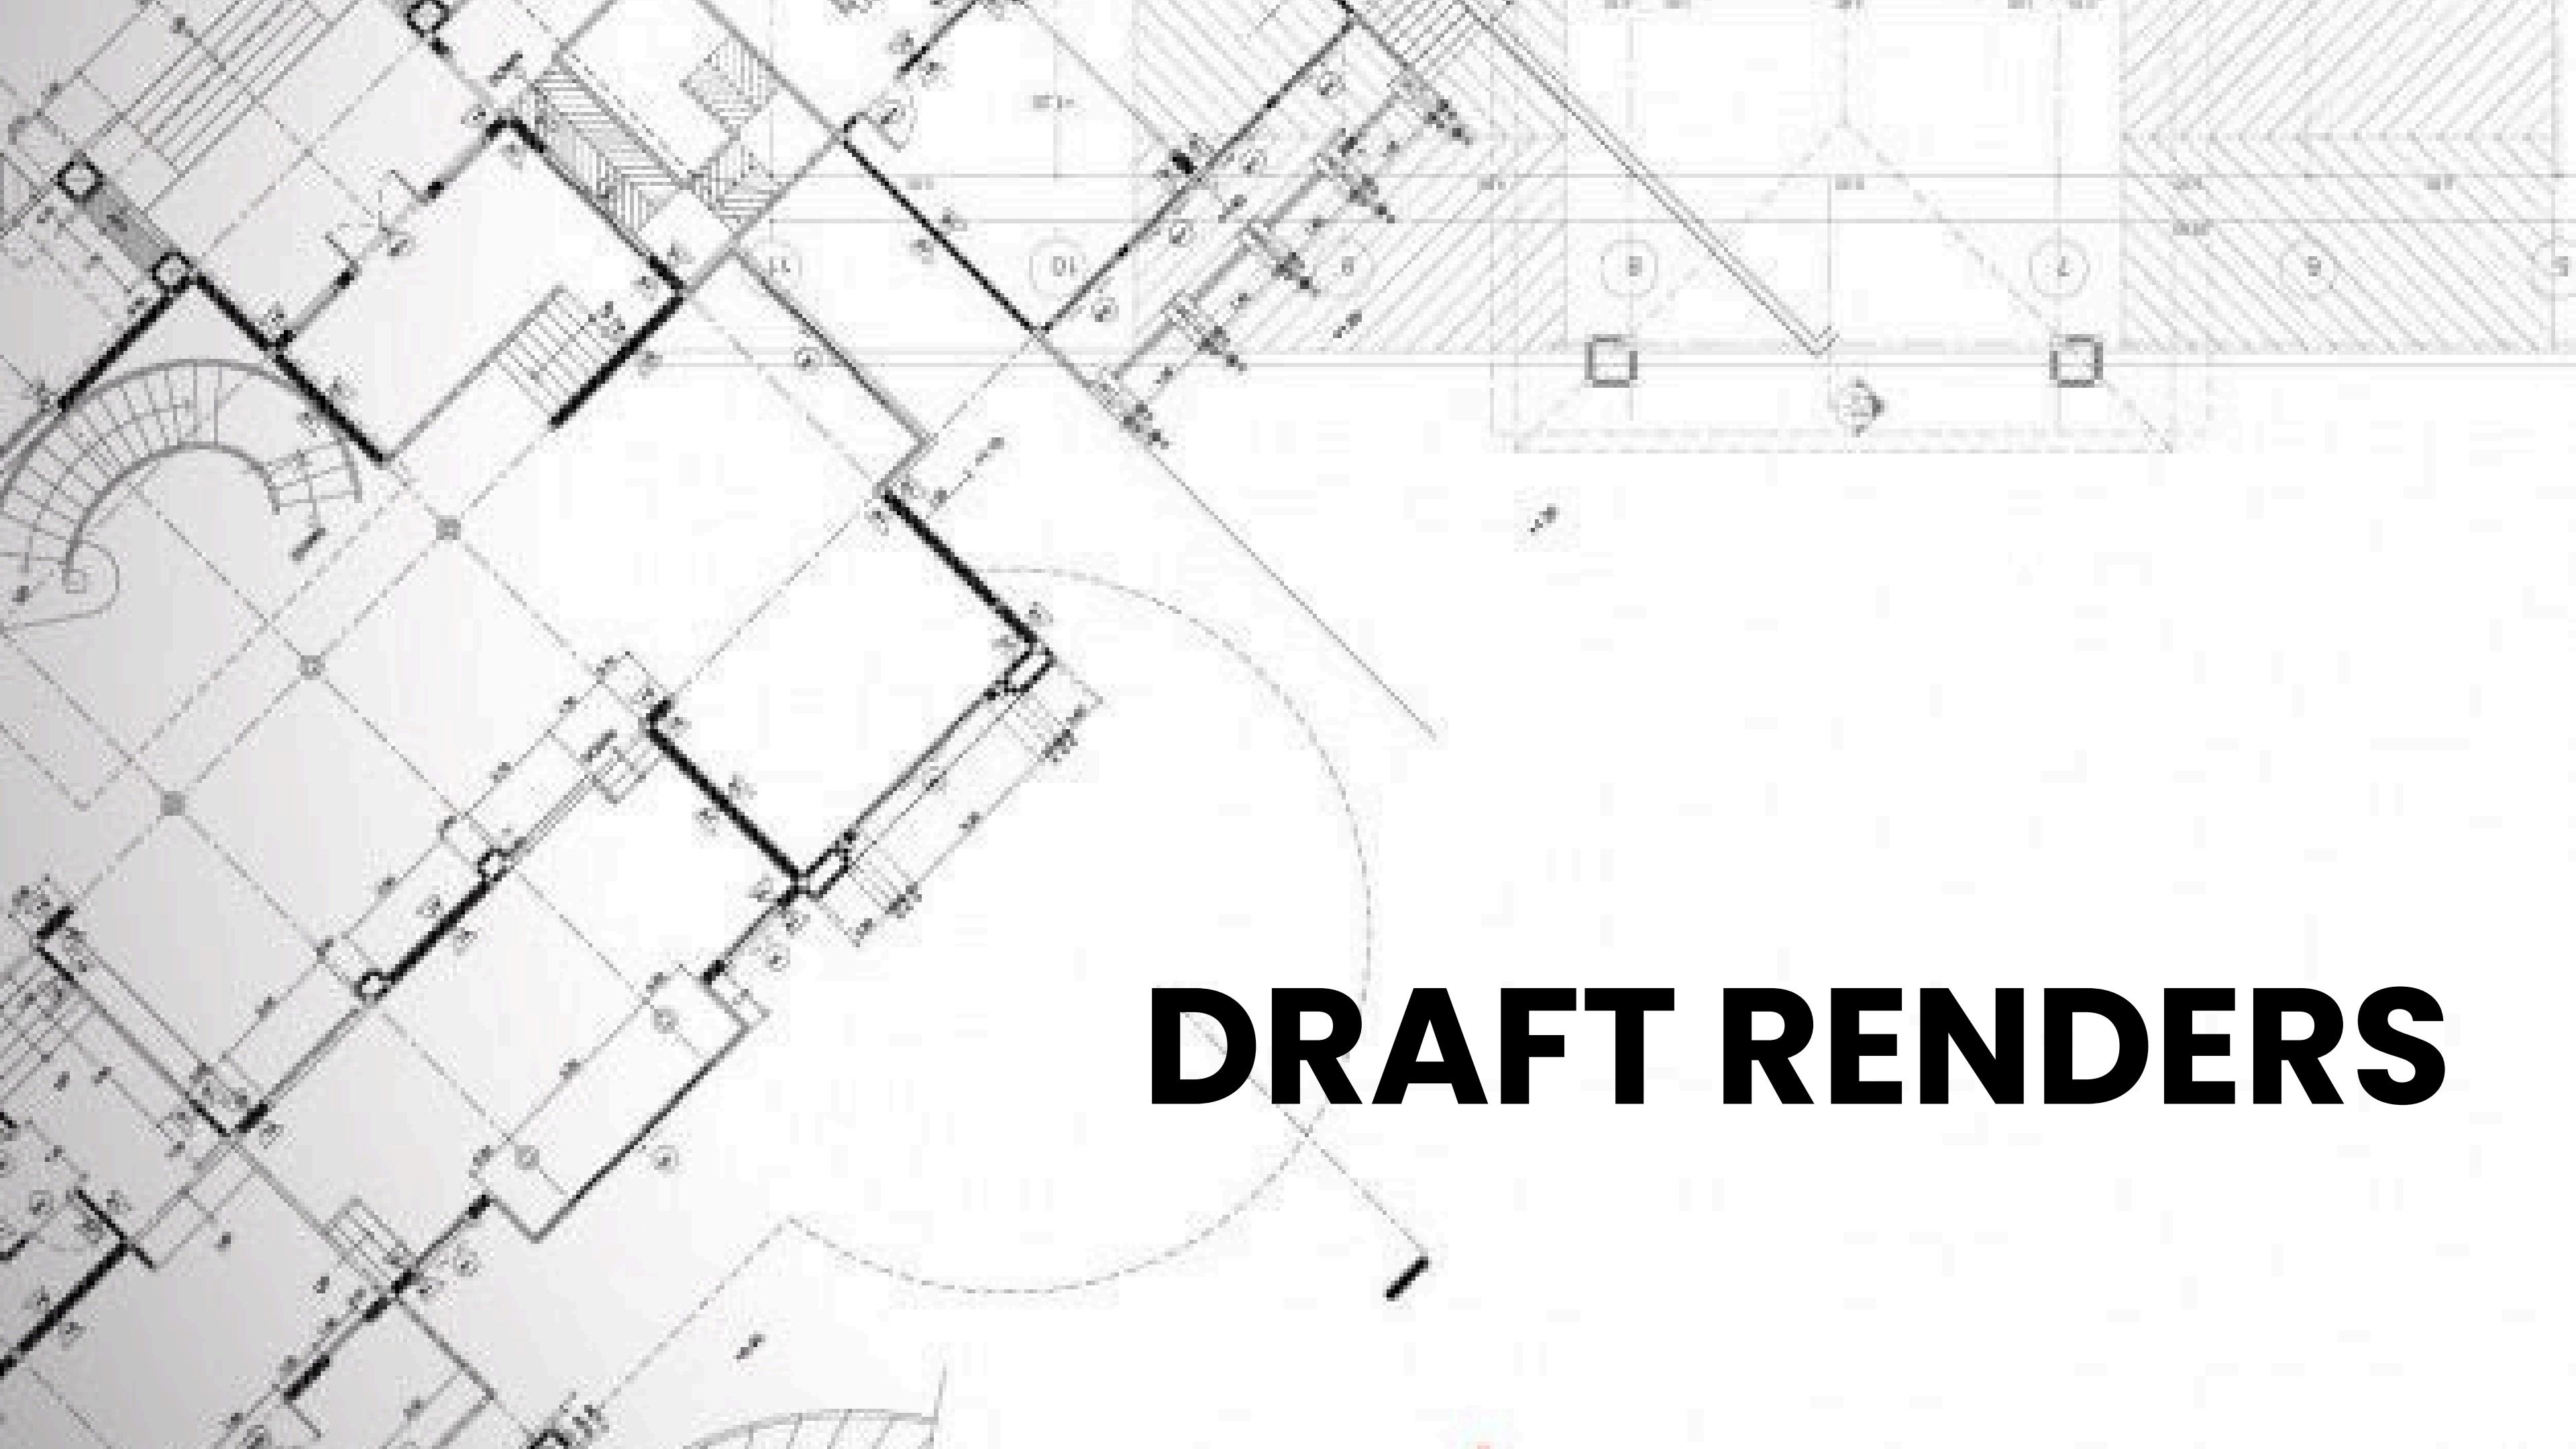A detailed black and white architectural floor plan of a building. The plan includes various rooms, windows, doors, and structural details. It features a grid system with horizontal and vertical lines, and some areas are shaded with cross-hatching. The text 'DRAFT RENDERS' is overlaid on the right side of the image.

DRAFT RENDERS

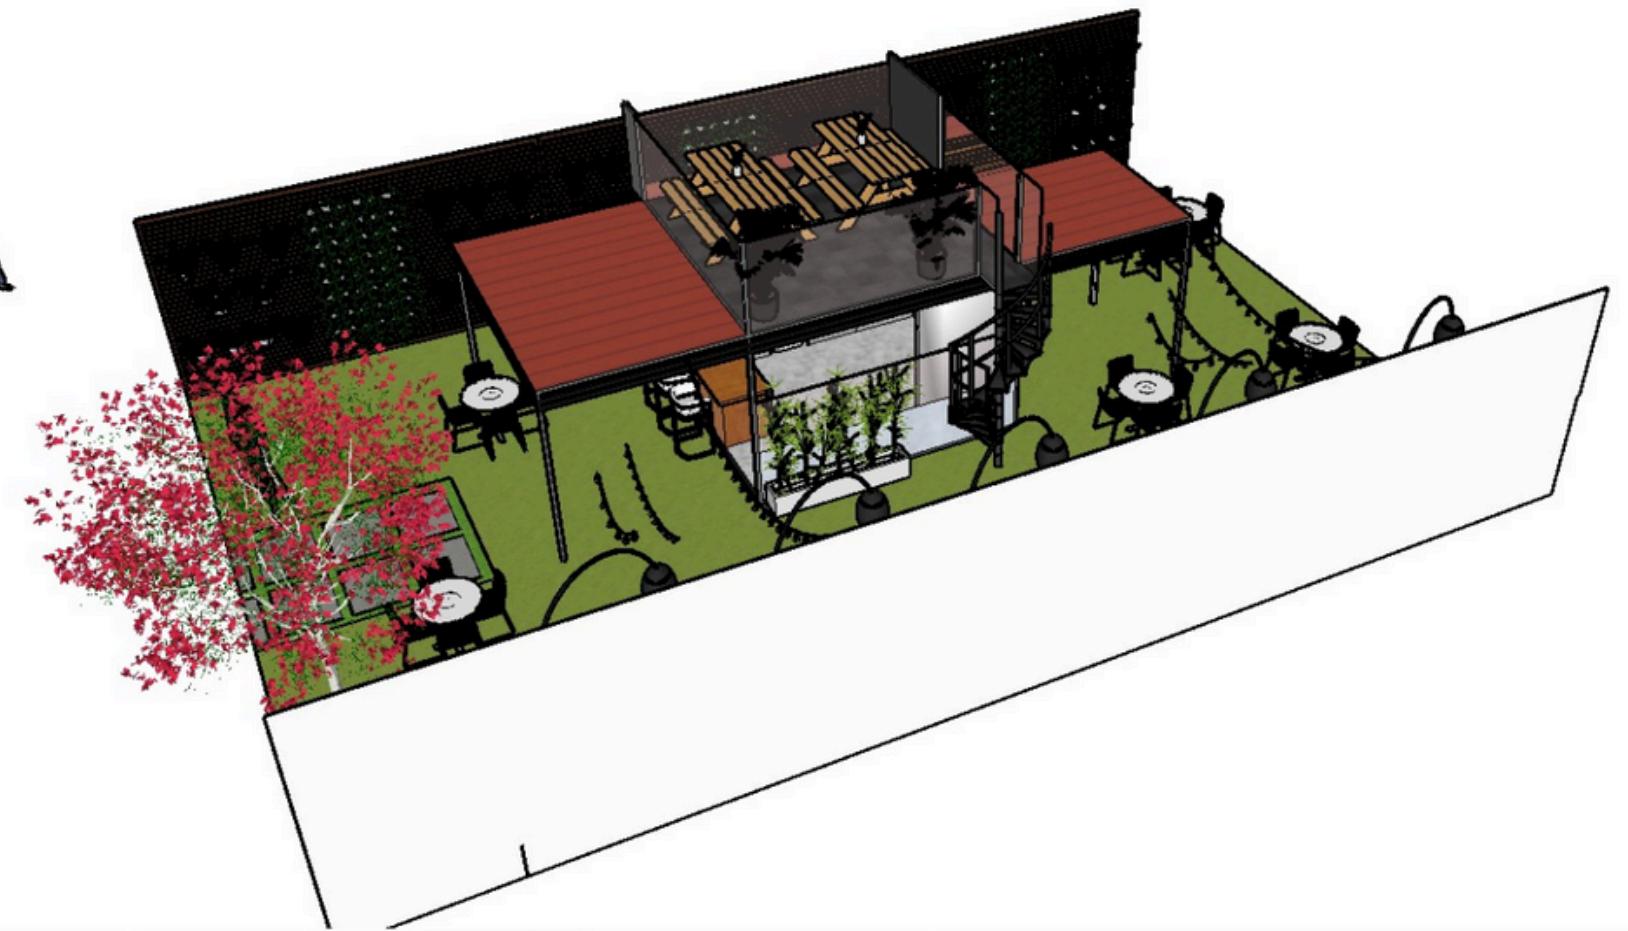

CAFE

LET'S WORK
TOGETHER
